GENERAL NOTES
1. CONCRETE: C30/37, EXPOSURE CLASS XC1.
2. REINFORCEMENT: B500B, T = HIGH-YIELD.
3. NOMINAL COVER TO LINKS: 40 mm.
4. LAPS: 50 x BAR DIAMETER UNLESS NOTED.
5. DO NOT SCALE. ALL DIMENSIONS IN mm.

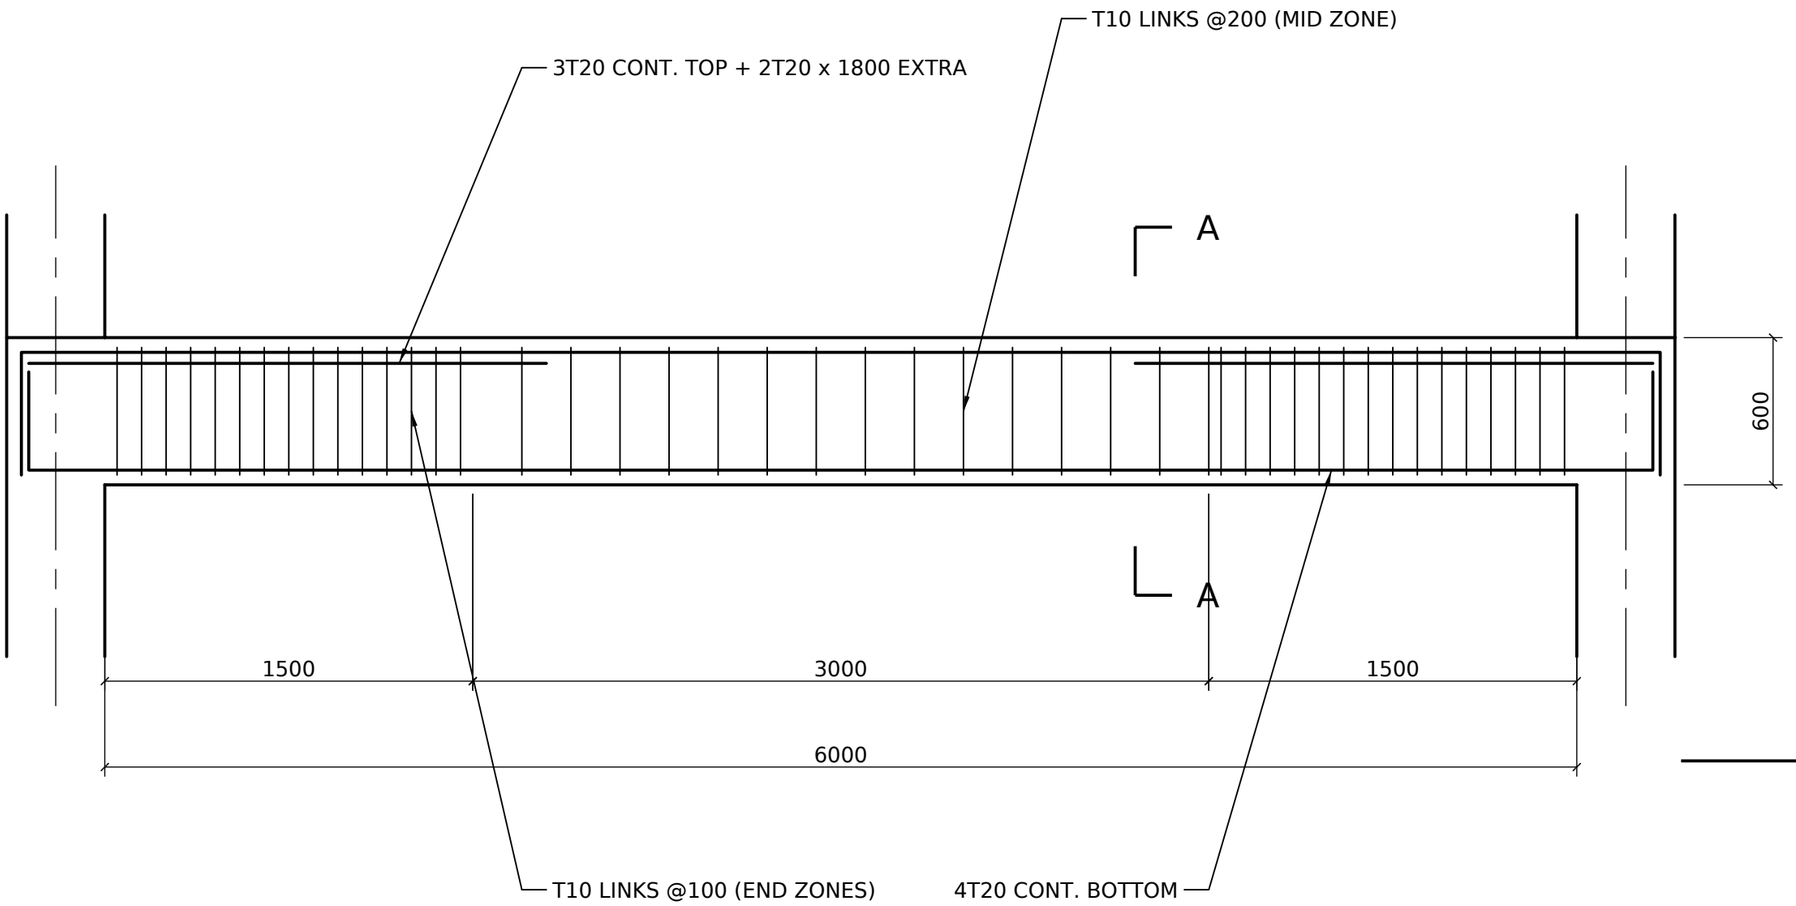

BEAM B1 - ELEVATION

SCALE 1:25

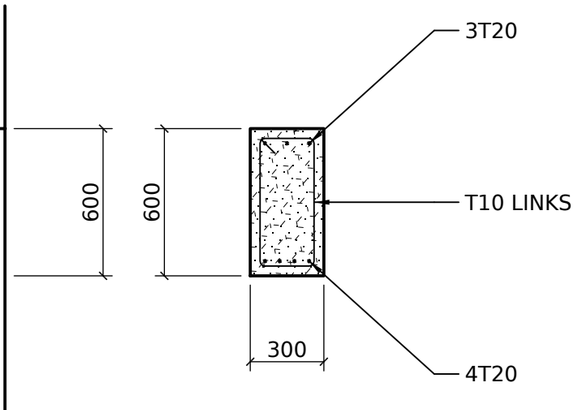

SECTION A-A

SCALE 1:25

SAMPLE OFFICE BLOCK - LEVEL 2 FRAMING	
BEAM B1 - REINFORCEMENT DETAILS	
DRAWN: AS CHECKED: -- DATE: 2026-10-22	DWG No. S-201
SCALE: 1:25 @ A3	REV A